Общие данные

Рабочая документация. Электроснабжение и электроосвещение корпуса 1.
Напряжение сети 380/220 В, система заземления TN-S.
Расчётная мощность Pр = 85,5 кВт, коэффициент мощности 0,92.
Электромонтажные работы выполнять по действующим нормам.


Ведомость листов

1 Общие данные
2 План освещения. Корпус 1, этаж 1
3 Схема электрическая принципиальная ЩО-1
4 Схема электрическая вводного устройства ВРУ-1
5 План силовых сетей. Корпус 1, этаж 1
6 План заземления. Корпус 1

Обозначение

СИНТ-01-ЭМ


Наименование листа	Стадия	Лист
Общие данные	Р	1
	Изм. Изм.0	Дата 15.01.2026
	Организация СИНТЕТИКПРОЕКТ	

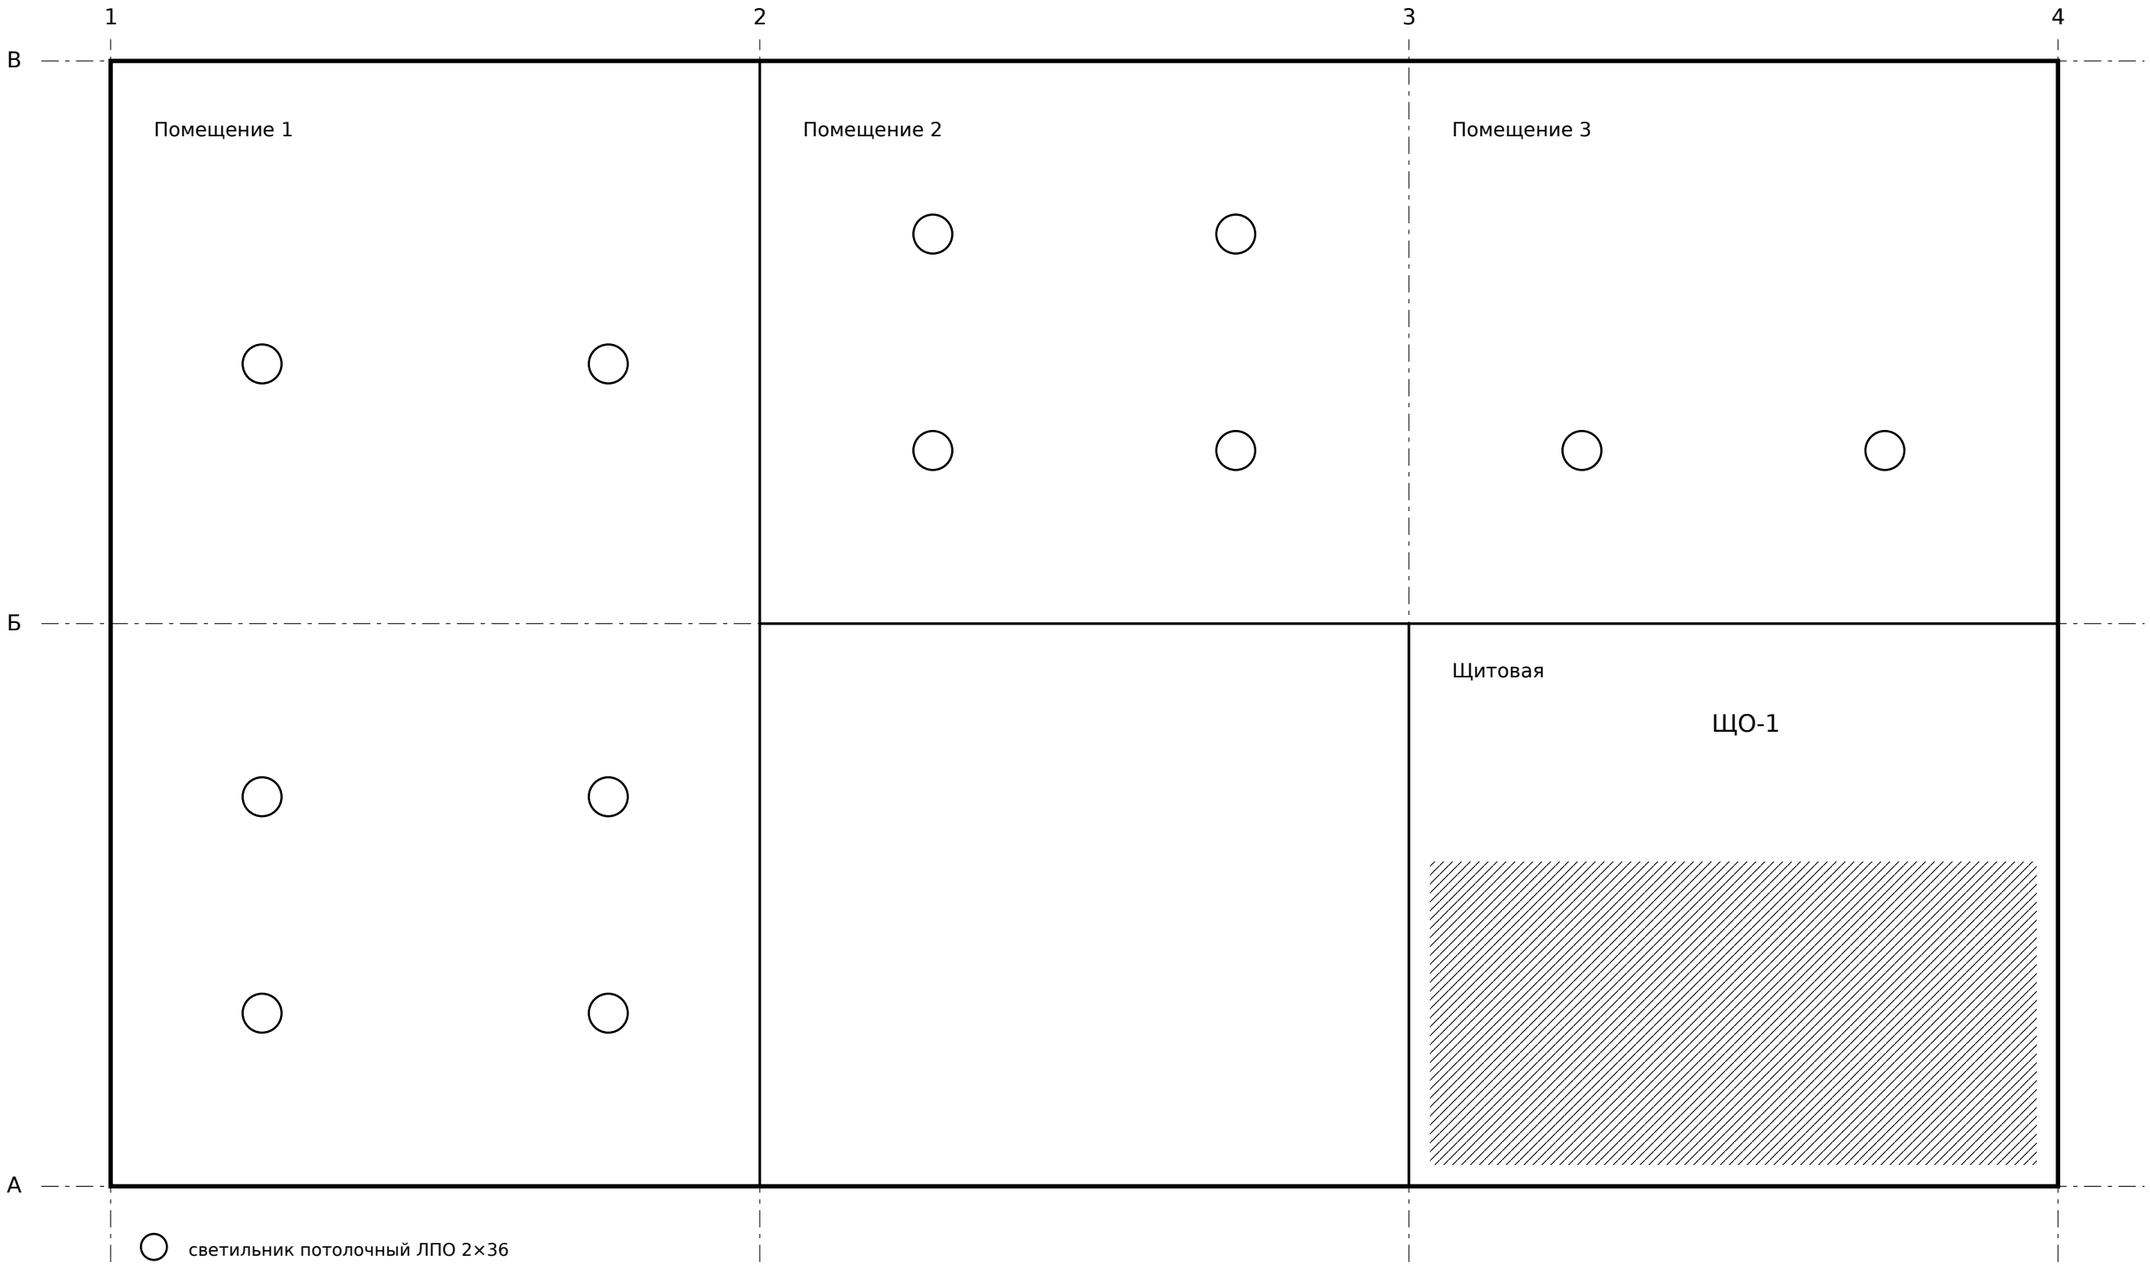

○ светильник потолочный ЛПО 2×36

Высота установки щита ЩО-1 — 1,5 м.
Степень защиты светильников IP20.

Обозначение: СИНТ-01-ЭМ		
Наименование листа: План освещения. Корпус 1, этаж 1	Стадия: Р	Лист: 2
	Изм.: Изм.1	Дата: 12.02.2026
	Организация: СИНТЕТИКПРОЕКТ	

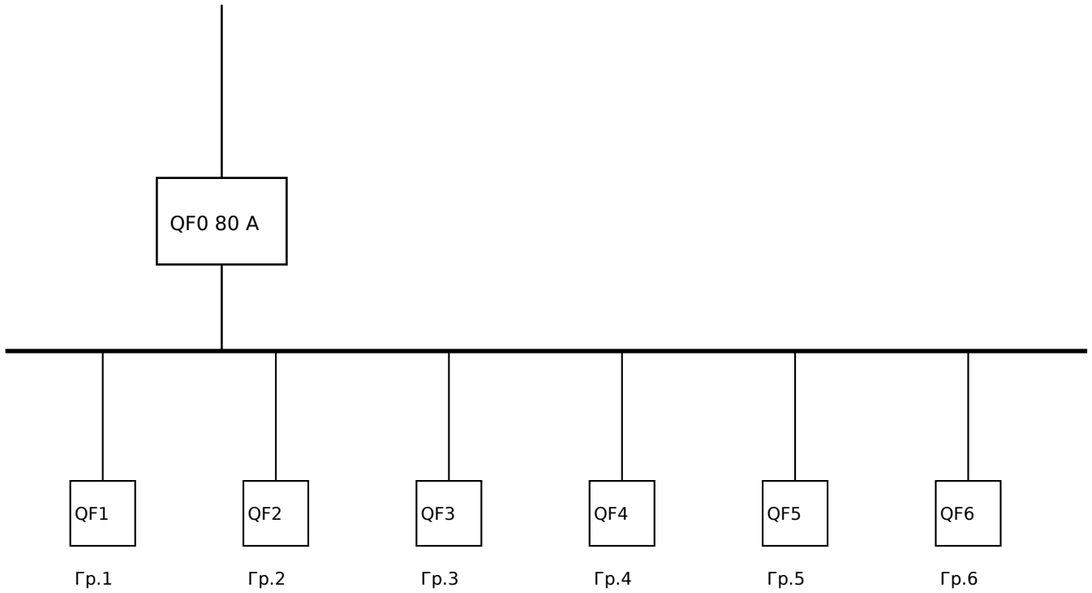

№ гр.	Нагрузка, кВт	Кабель	Автомат, А
1	1,2	ВВГнг 3×1,5	16
2	2,4	ВВГнг 3×2,5	25
3	3,6	ВВГнг 3×2,5	32
4	1,8	ВВГнг 3×1,5	16
5	4,5	ВВГнг 3×4	40
6	0,8	ВВГнг 3×1,5	10

Обозначение

СИНТ-01-ЭМ


Наименование листа

Схема электрическая принципиальная ЩО-1

Стадия	Лист
Р	3
Изм.	Дата
Изм.1	12.02.2026

Организация

СИНТЕТИКПРОЕКТ

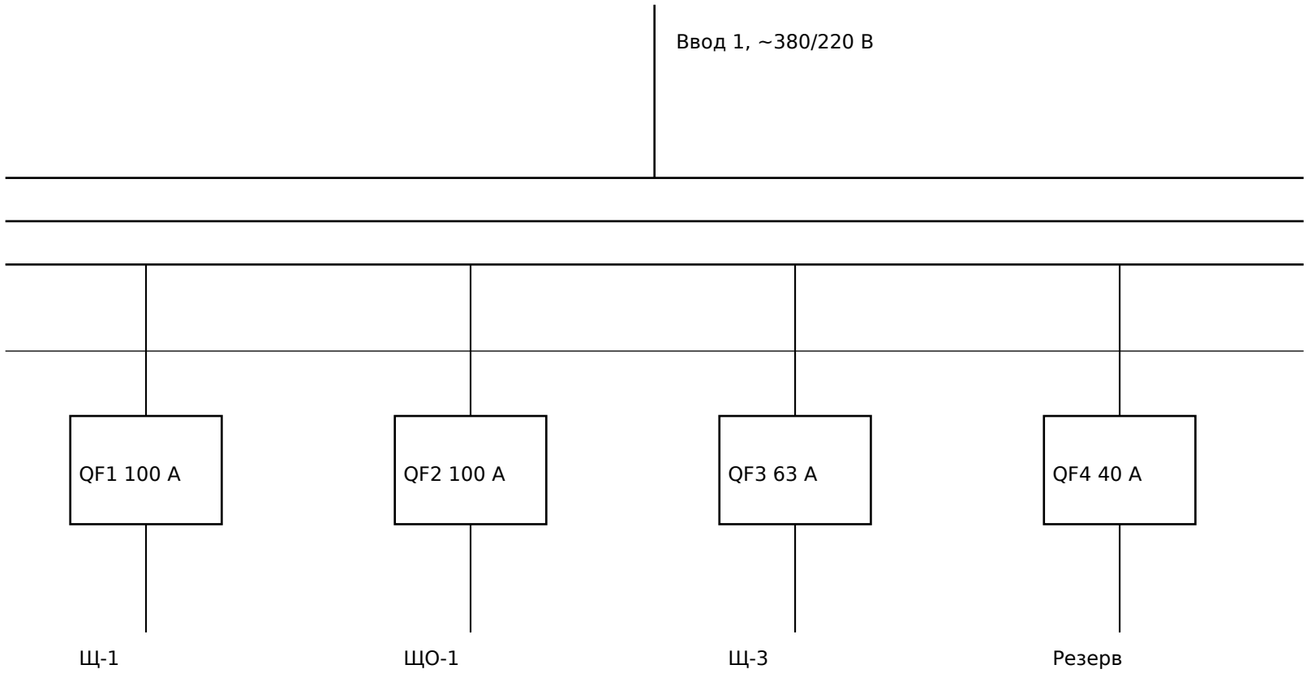

Все аппараты — на DIN-рейке, степень защиты щита IP31.

Обозначение: СИНТ-01-ЭМ		
Наименование листа: Схема электрическая вводного устройства ВРУ-1	Стадия: Р	Лист: 4
	Изм.: Изм.1	Дата: 12.02.2026
	Организация: СИНТЕТИКПРОЕКТ	

Цех 1 (L)


Склад (L)

Бытовые помещения (L)

Насосная (L)

Венткамера (L)

Щитовая (L)

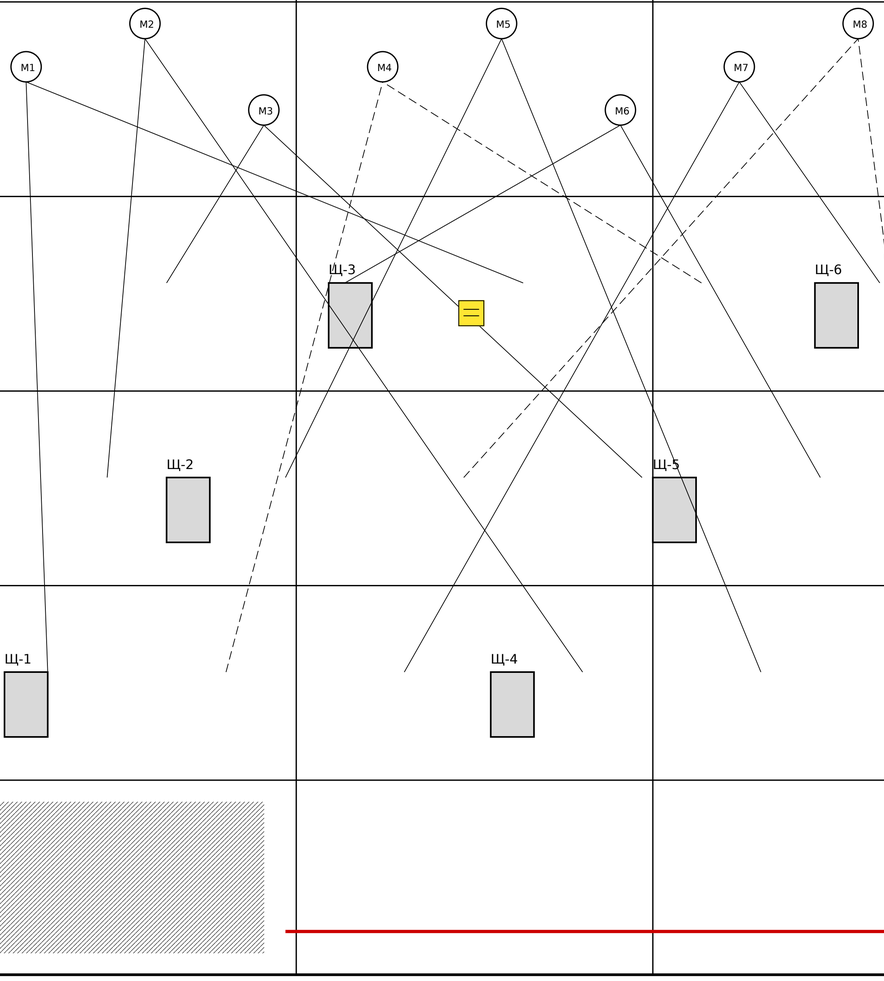

Цех 1 (R)


Склад (R)

Бытовые помещения (R)

Насосная (R)

Венткамера (R)

Щитовая (R)

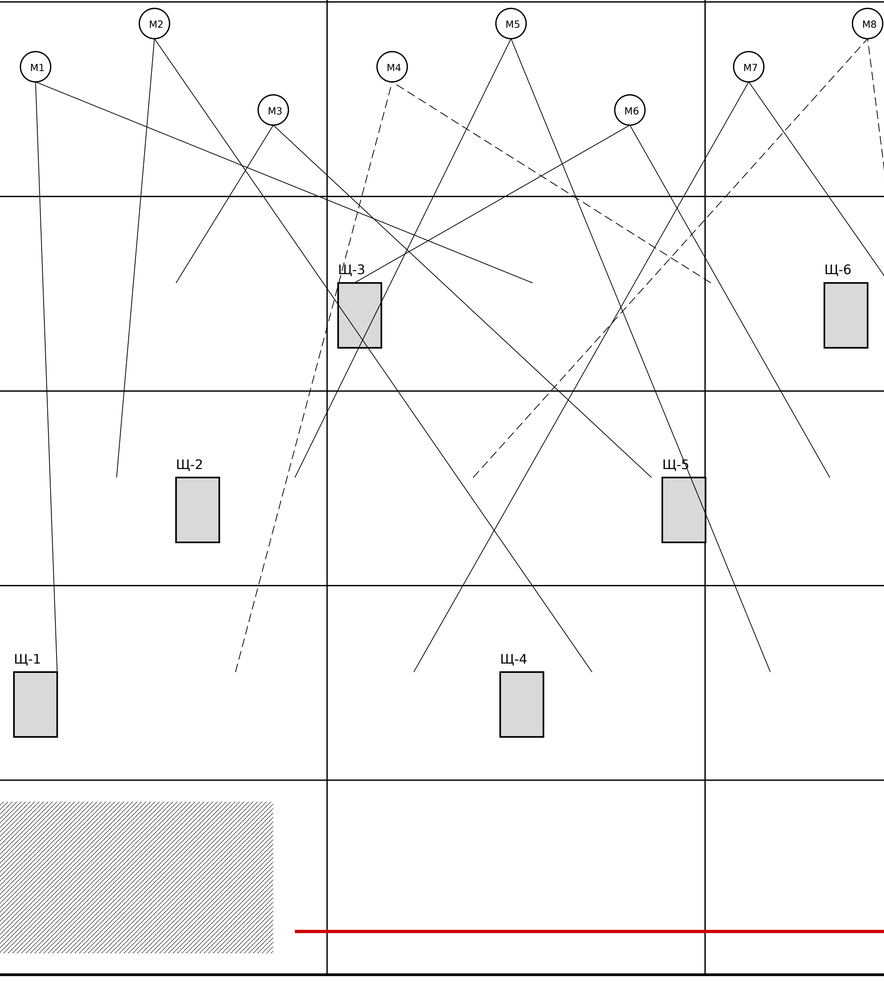

Обозначение

СИНТ-01-ЭМ


Наименование листа

План силовых сетей. Корпус 1, этаж 1

Стадия	Лист
Р	5
Изм.	Дата
Изм.0	15.01.2026

Организация

СИНТЕТИКПРОЕКТ

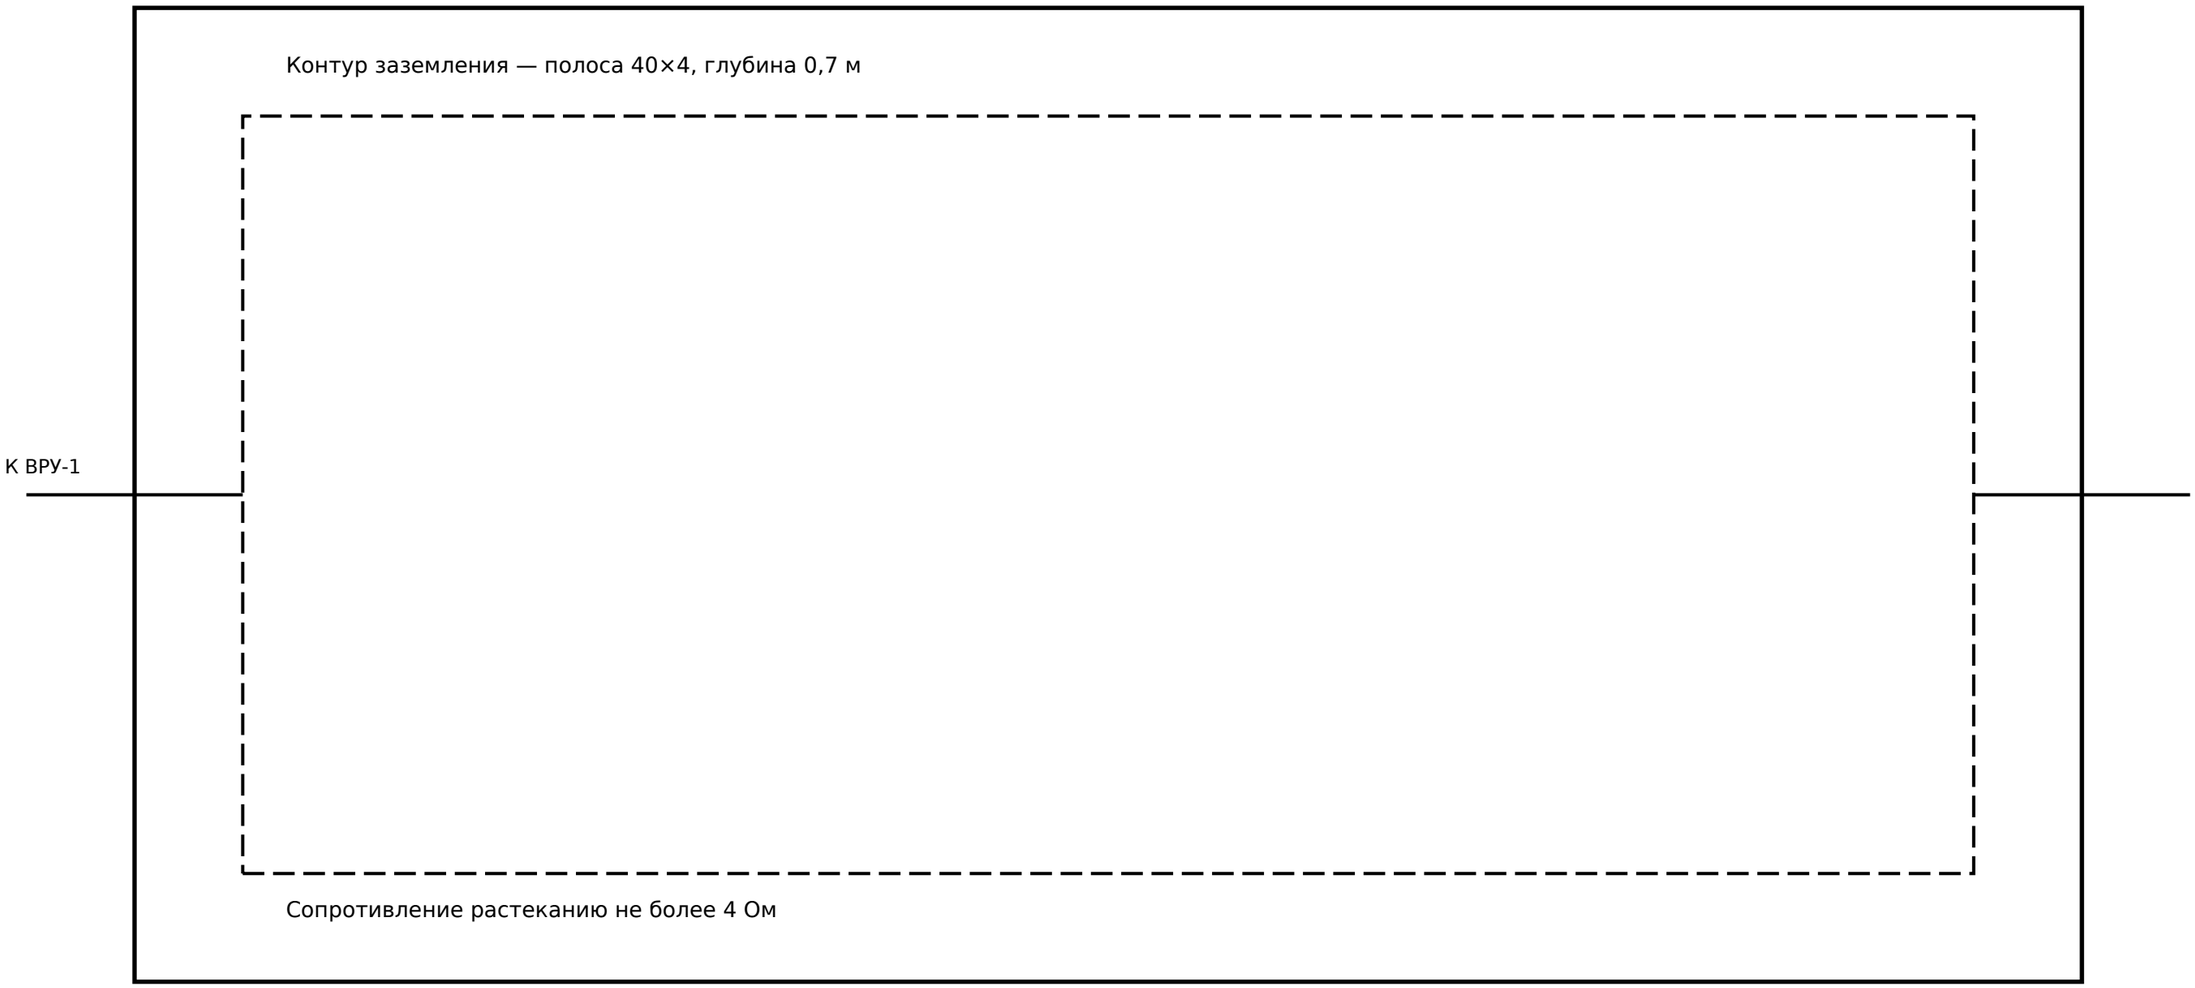

Обозначение

СИНТ-01-ЭМ

Наименование листа	Стадия	Лист
План заземления. Корпус 1	Р	6
	Изм.	Дата
	Изм.0	15.01.2026
	Организация	
	СИНТЕТИКПРОЕКТ	