Общие данные

Рабочая документация. Электроснабжение и электроосвещение корпуса 1.
Напряжение сети 380/220 В, система заземления TN-S.
Расчётная мощность Pр = 85,5 кВт, коэффициент мощности 0,92.
Электромонтажные работы выполнять по действующим нормам.

Ведомость листов

1 Общие данные
2 План освещения. Корпус 1, этаж 1
3 Схема электрическая принципиальная ЩО-1
4 Схема электрическая вводного устройства ВРУ-1
5.1 План силовых сетей. Корпус 1, этаж 1 (часть 1)
5.2 План силовых сетей. Корпус 1, этаж 1 (часть 2)
7 Спецификация оборудования, изделий и материалов


Разрешение на внесение изменений

Изм.	Лист	Содержание изменения
3	5	Дополнена трасса кабельного лотка
3	7	Изменено сечение кабеля, поз. 4
3	4	QF2 заменён: 100 А на 125 А

Обозначение

СИНТ-01-ЭМ


Наименование листа	Стадия	Лист
Общие данные	Р	1
	Изм. Изм.4	Дата 05.05.2026
	Организация СИНТЕТИКПРОЕКТ	

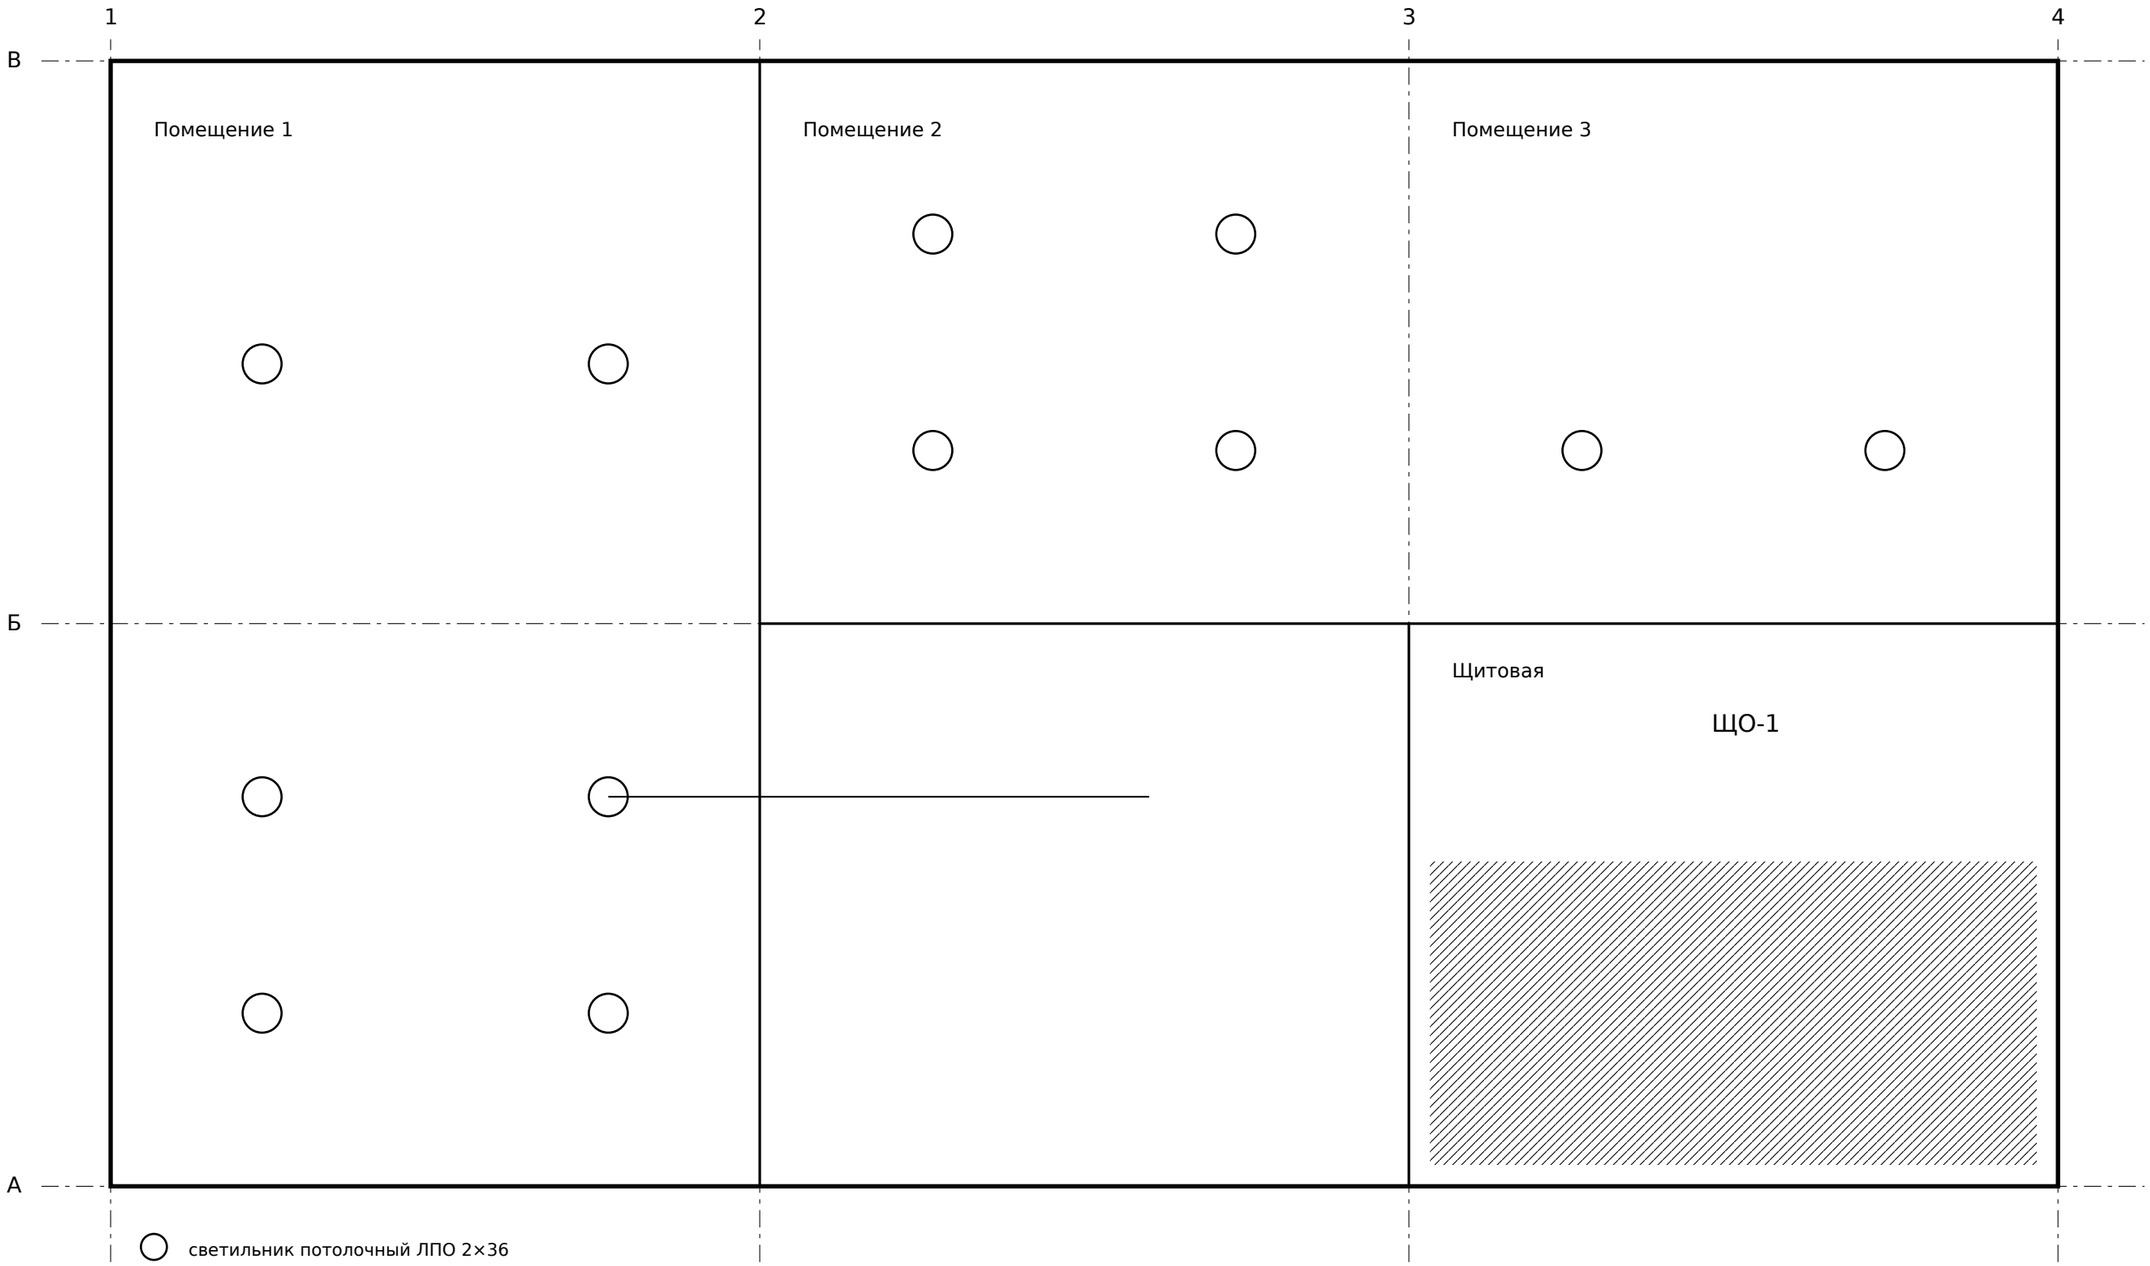

○ светильник потолочный ЛПО 2×36

Высота установки щита ЩО-1 — 1,5 м.
Степень защиты светильников IP20.

Обозначение: СИНТ-01-ЭМ		
Наименование листа: План освещения. Корпус 1, этаж 1	Стадия: Р	Лист: 2
	Изм.: Изм.2	Дата: 10.03.2026
	Организация: СИНТЕТИКПРОЕКТ	

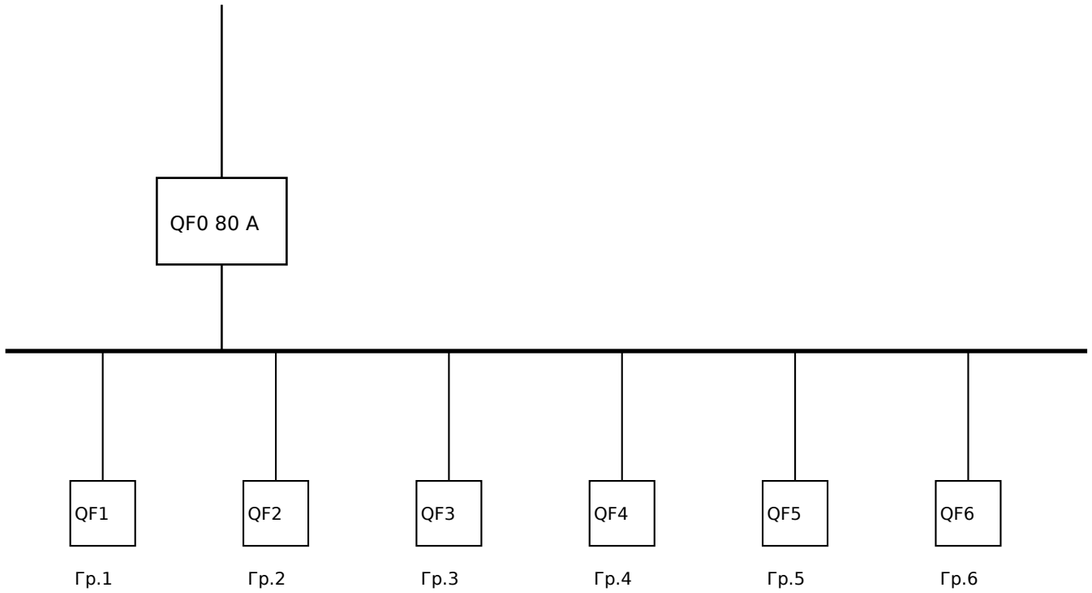

№ гр.	Нагрузка, кВт	Кабель	Автомат, А
1	1,2	ВВГнг 3×1,5	16
2	2,4	ВВГнг 3×4	25
3	3,6	ВВГнг 3×2,5	32
4	1,8	ВВГнг 3×1,5	16
5	4,5	ВВГнг 3×4	40
6	0,8	ВВГнг 3×1,5	10

Обозначение

СИНТ-01-ЭМ


Наименование листа

Схема электрическая принципиальная ЩО-1

Стадия	Лист
Р	3
Изм.	Дата
Изм.1	12.02.2026

Организация

СИНТЕТИКПРОЕКТ

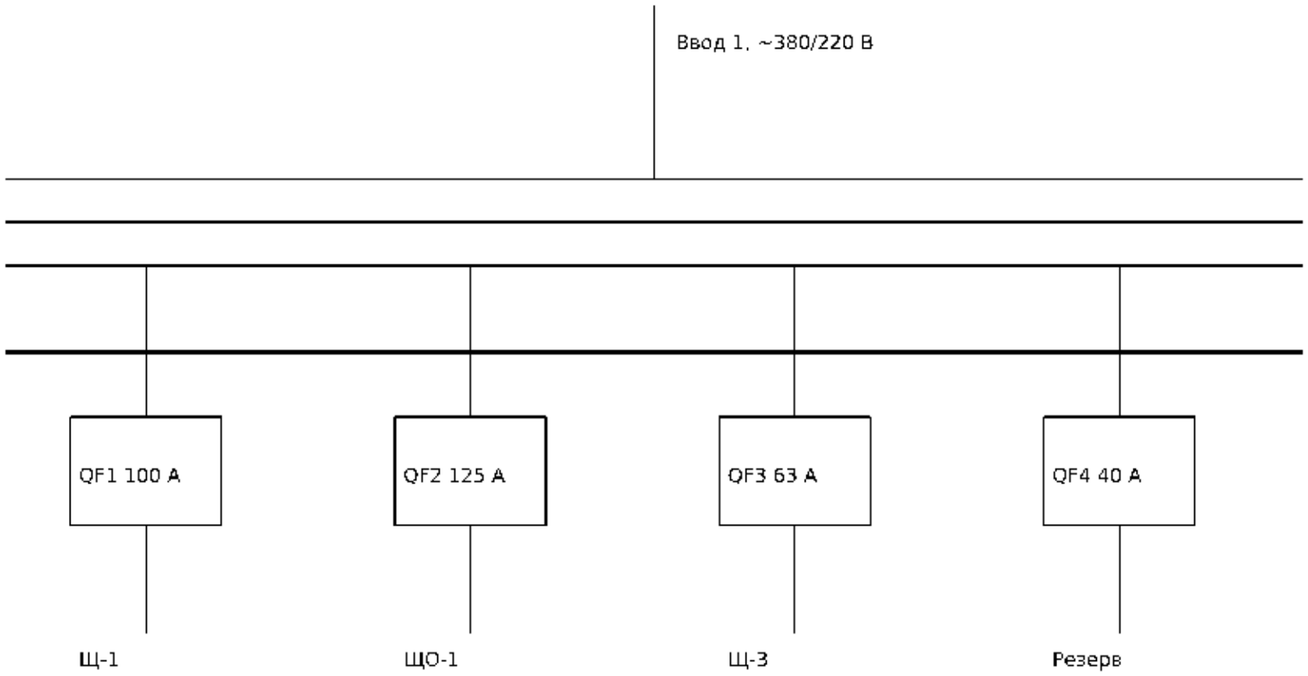

Все аппараты — на DIN-рейке, степень защиты щита IP31.

Обозначение

СИНТ-01-ЭМ

Наименование листа

Схема электрическая вводного устройства ВРУ-1

Стадия	Лист
Р	4
Изм.	Дата
Изм.3	07.04.2026

Организация

СИНТЕТИКПРОЕКТ

Цех 1 (L)


Склад (L)

Бытовые помещения (L)

Насосная (L)

Венткамера (L)

Щитовая (L)

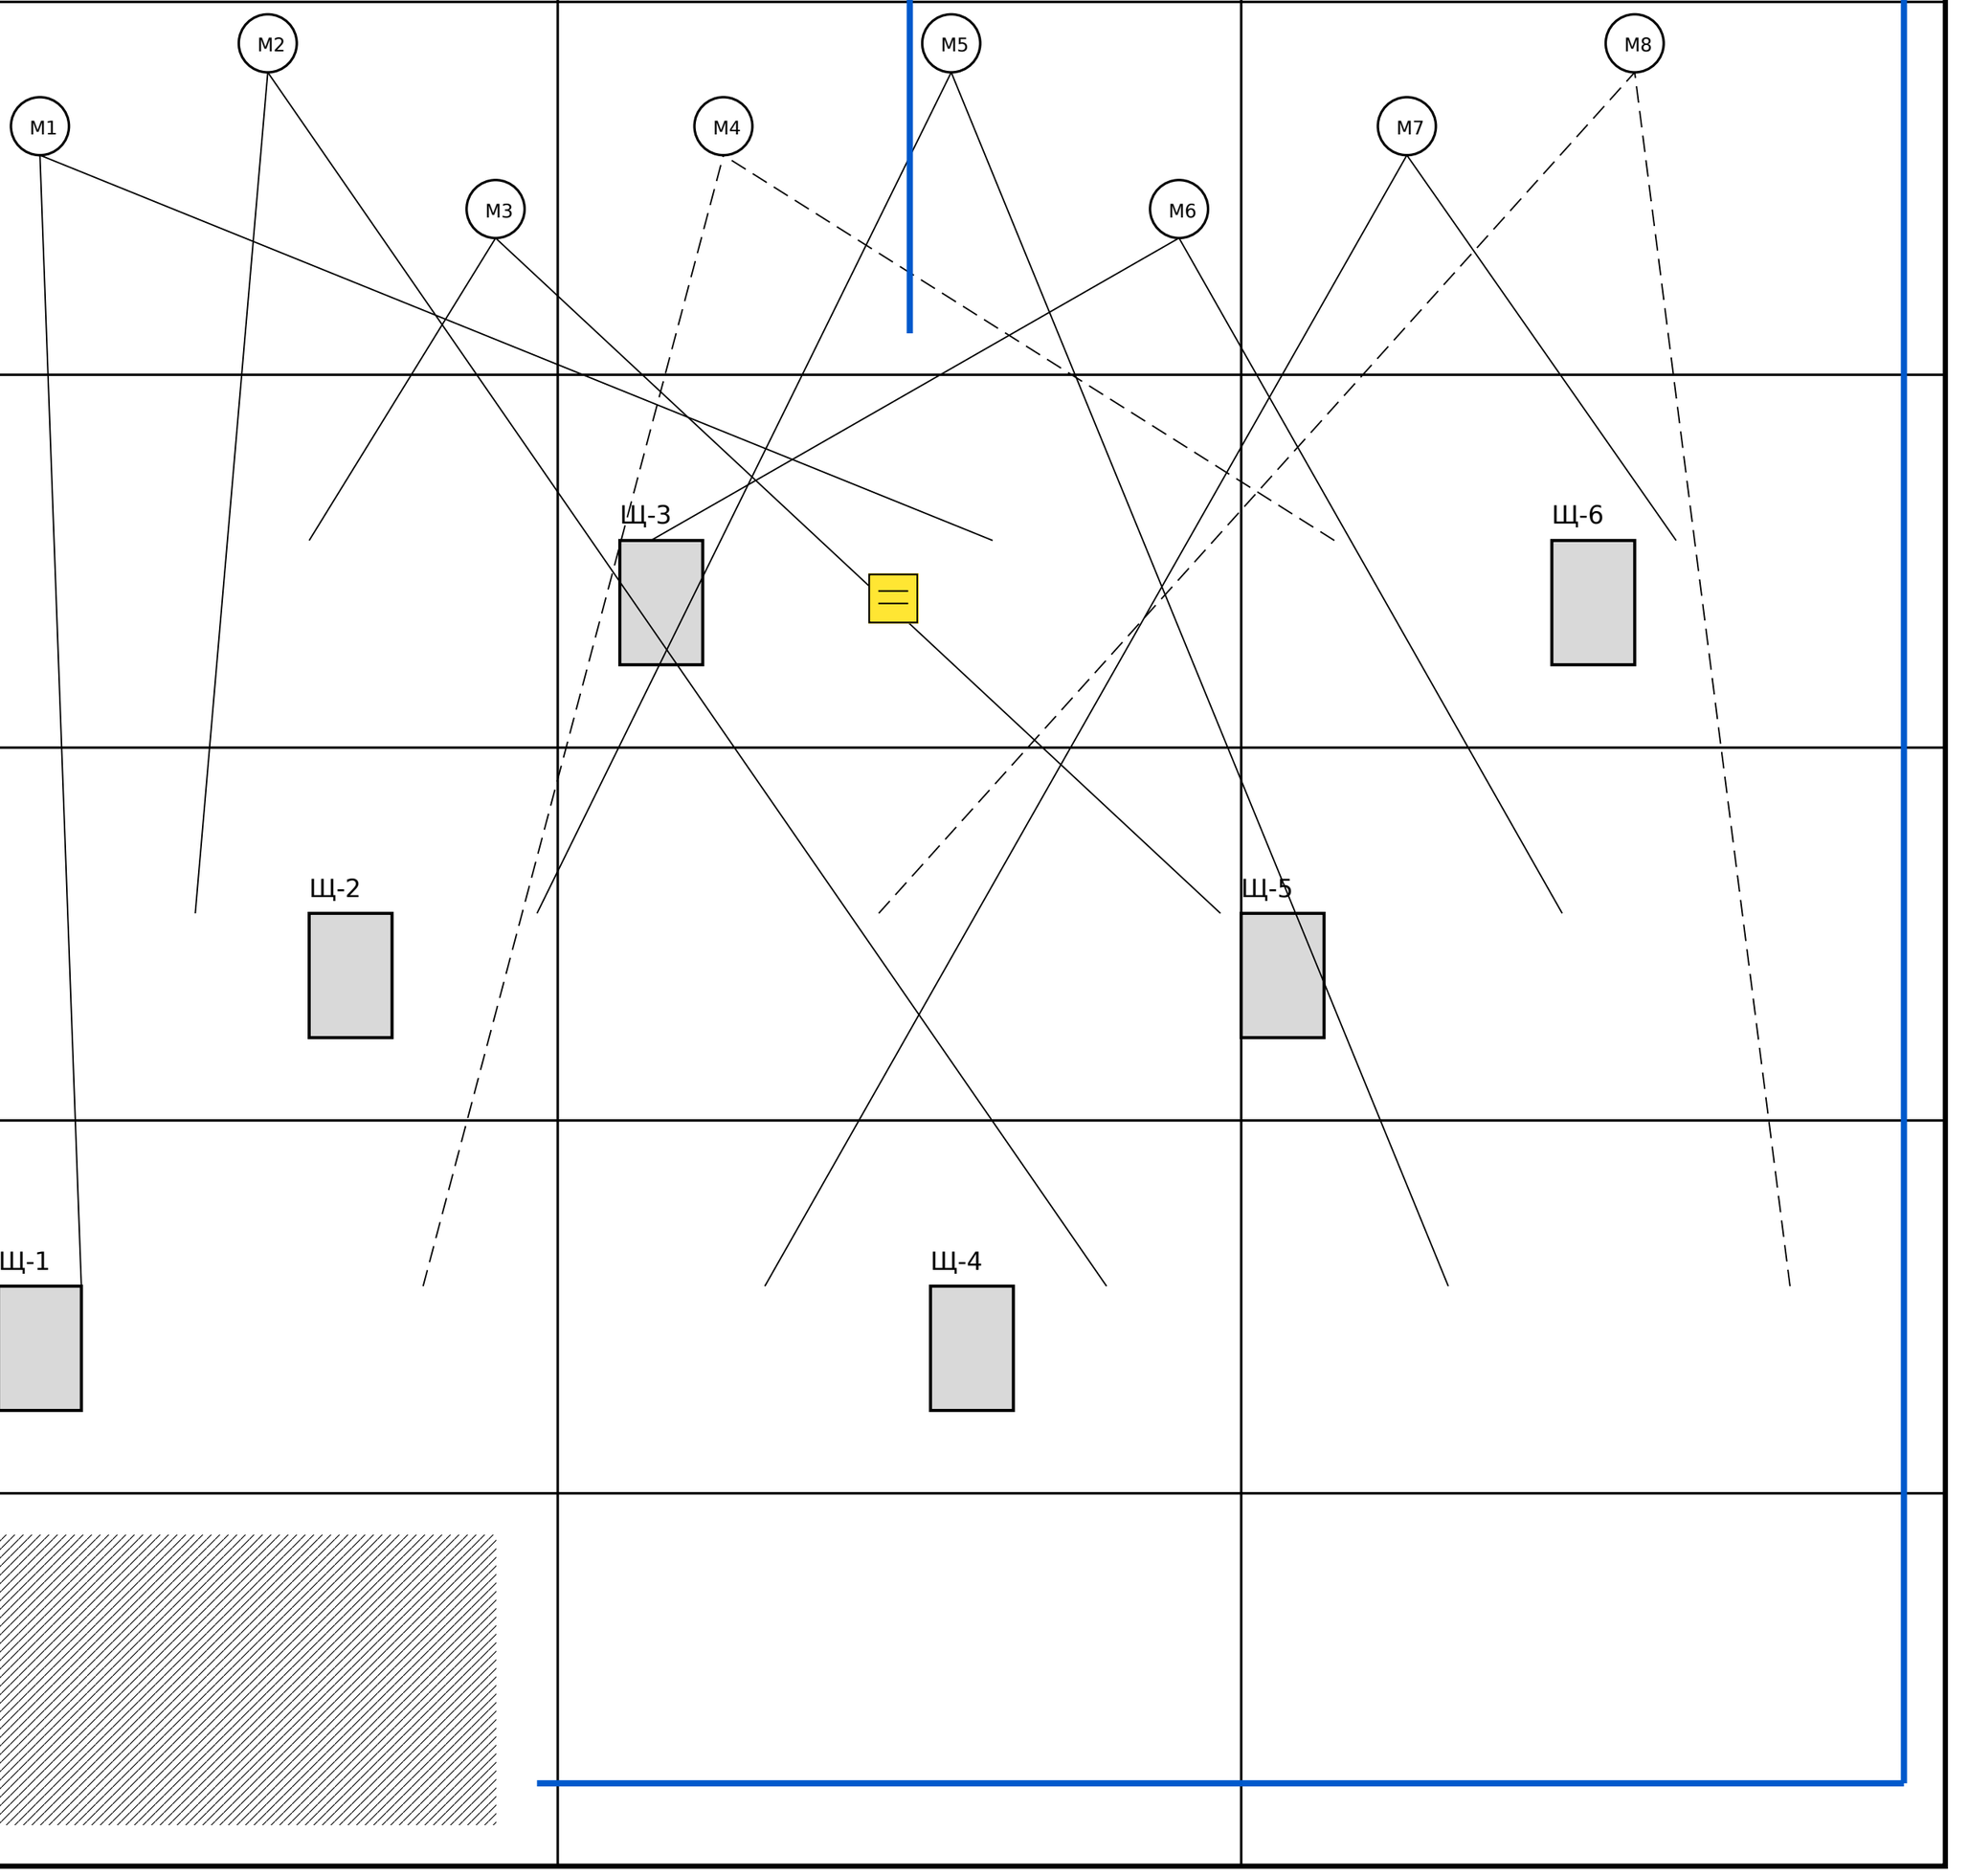

Обозначение	СИНТ-01-ЭМ
Наименование листа	План силовых сетей. Корпус 1, этаж 1 (часть 1)
Стадия	Р
Лист	5.1
Изм.	Изм.4
Дата	05.05.2026
Организация	СИНТЕТИКПРОЕКТ

Цех 1 (R)


Склад (R)

Бытовые помещения (R)

Насосная (R)

Венткамера (R)

Щитовая (R)

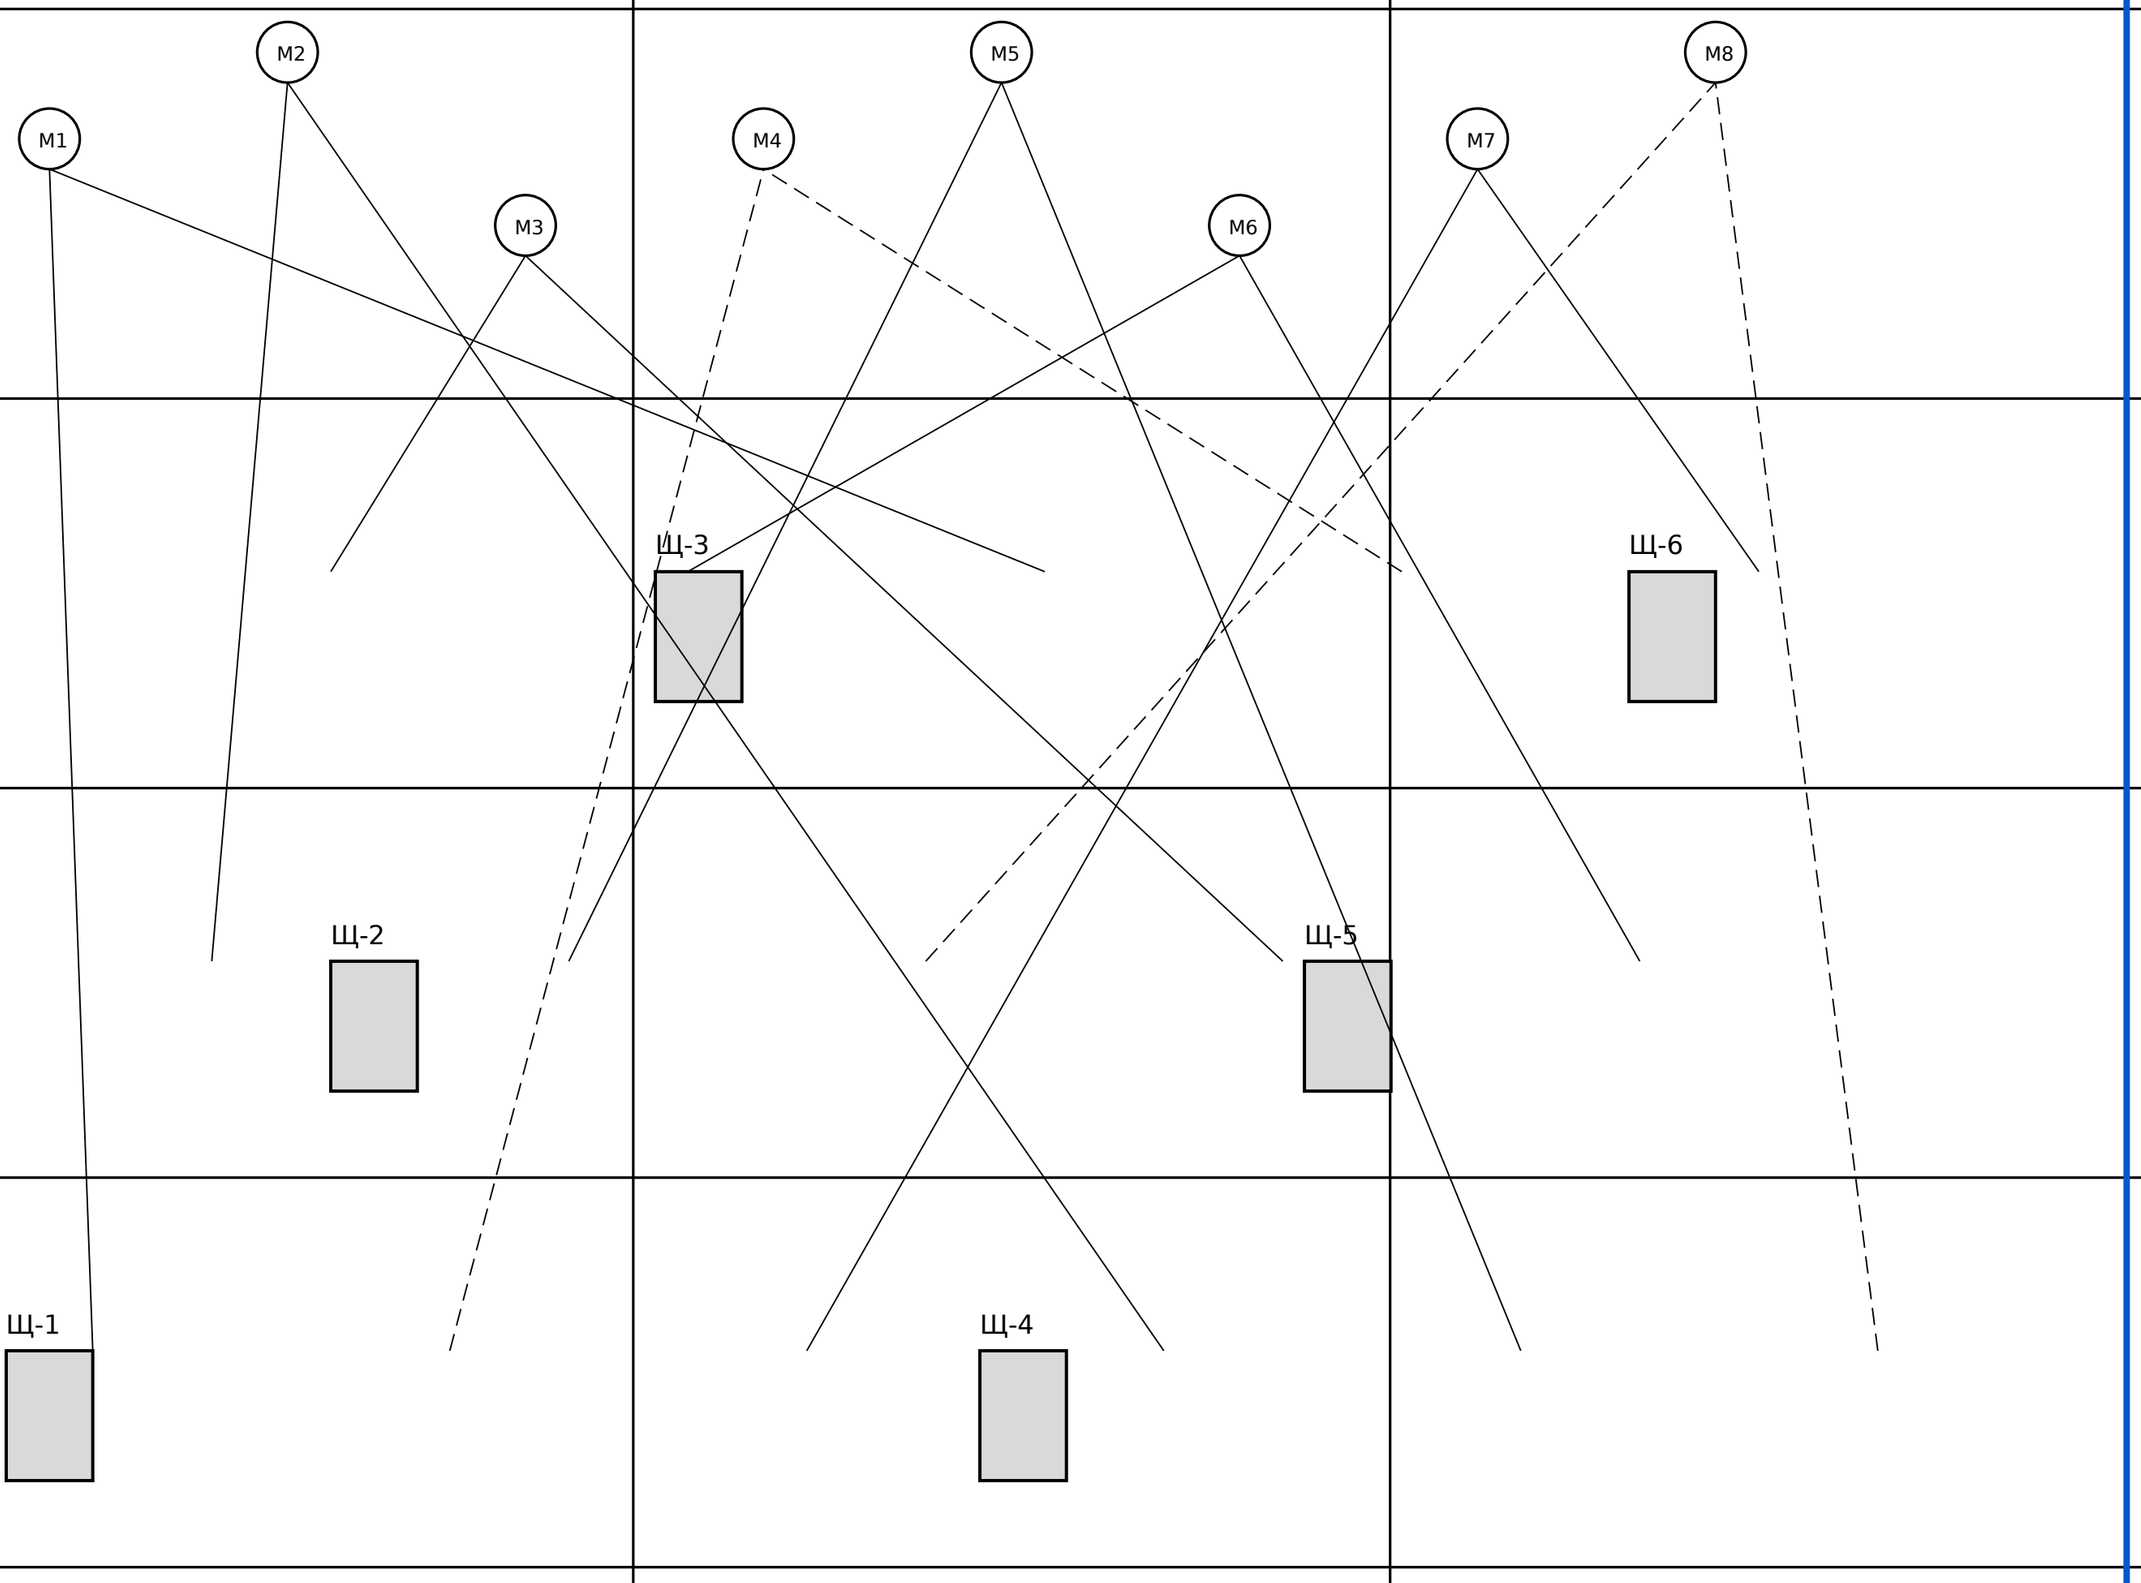

Обозначение	СИНТ-01-ЭМ
Наименование листа	План силовых сетей. Корпус 1, этаж 1 (часть 2)
Стадия	Р
Лист	5.2
Изм.	Изм.4
Дата	05.05.2026
Организация	СИНТЕТИКПРОЕКТ

Спецификация оборудования, изделий и материалов

Поз.	Обозначение	Наименование и тех. характеристика	Кол.	Масса ед., кг	Прим.
1	СИНТ-ЩО.01	Щит освещения ЩО-1	1	45,0	
2	СИНТ-АВ.16	Выключатель автоматический 16 А	12	0,15	
3	СИНТ-АВ.63	Выключатель автоматический 63 А	3	0,45	
4	СИНТ-КБ.325	Кабель ВВГнг 3×2,5, м	320	0,12	
5	СИНТ-СВ.236	Светильник ЛПО 2×36	24	3,2	
7	СИНТ-СД.40	Светильник светодиодный 40 Вт	6	1,4	

Примечание: масса единицы указана справочно.

Обозначение

СИНТ-01-ЭМ


Наименование листа

Спецификация оборудования, изделий и материалов

Стадия	Лист
Р	7
Изм.	Дата
Изм.4	05.05.2026

Организация

СИНТЕТИКПРОЕКТ

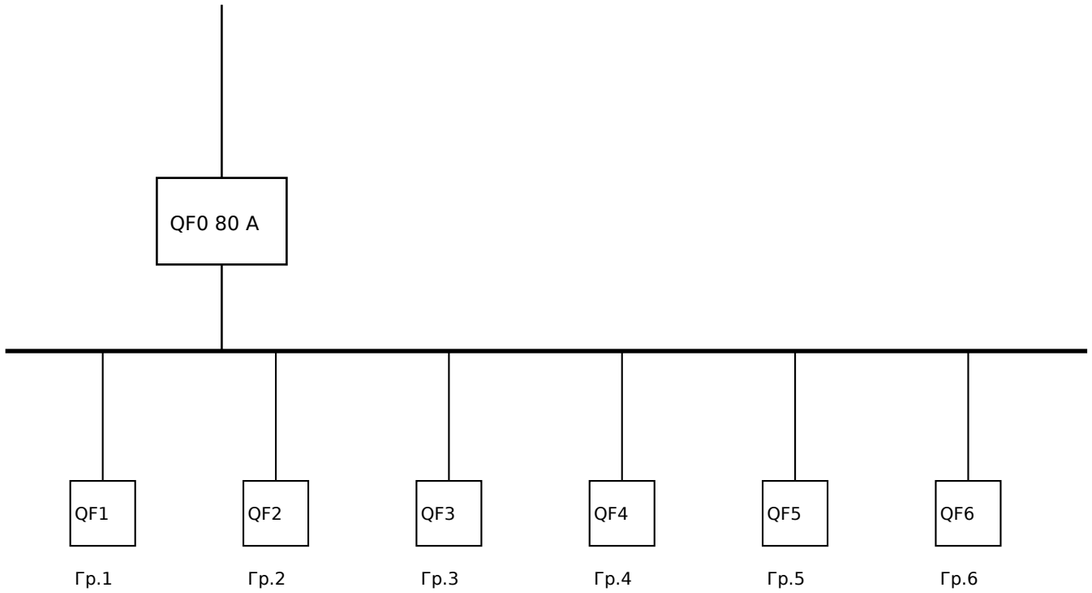

№ гр.	Нагрузка, кВт	Кабель	Автомат, А
1	1,2	ВВГнг 3×1,5	16
2	2,4	ВВГнг 3×4	25
3	3,6	ВВГнг 3×2,5	32
4	1,8	ВВГнг 3×1,5	16
5	4,5	ВВГнг 3×4	40
6	0,8	ВВГнг 3×1,5	10

Обозначение

СИНТ-01-ЭМ

Наименование листа

Схема электрическая принципиальная ЩО-1

Стадия	Лист
Р	3
Изм.	Дата
Изм.1	12.02.2026

Организация

СИНТЕТИКПРОЕКТ